

C A M P A N A



A R C H I T E C T U R E

OPERATION

RESTRUCTURATION D'UN APPARTEMENT

Section AH - Parcelle N°124

51 Rue d'Italie – 13 100 Aix en Provence

MAITRE D'OUVRAGE

SCI CHIARA

Représentée par Mr GRIMALDI Ange-Paul

20 229 CAMPANA

MAITRISE D'OEUVRE


FRANCOIS CAMPANA ARCHITECTE D.P.L.G.

11, Avenue Napoléon III immeuble le « Corse »

20 000 AJACCIO

Tél : 04.95.10.23.86

e.mail : campana.architecture@orange.fr

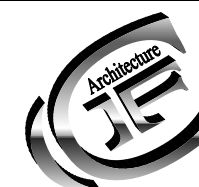

PLANS PHASE PRO

Janvier 2023

C A M P A N A

A R C H I T E C T U R E

COMMUNE D'AIX EN PROVENCE

ANGE PAUL GRIMALDI
51, Rue d'Italie


ETAT DES LIEUX

Cadastre : Section AH parcelle 124.

Echelle 1/100


Le 24/11/2022
Dossier : 8948_INT

Echelle 1/100

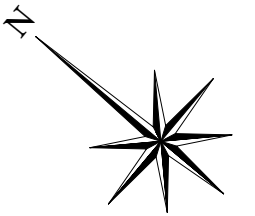

Légende:

Application cadastrale

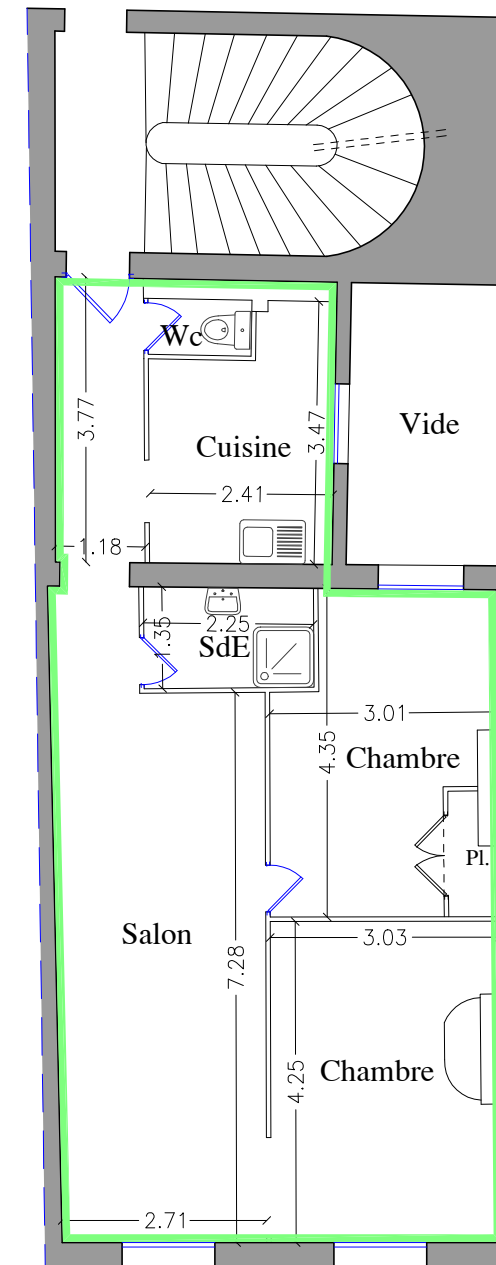


Rue d'Italie

0m 1m 5m

Surface : 62,0 m²

NOTE AUX ENTREPRISES :

La structure porteuse ne devra en aucun cas être demolie ou modifiée.
Avant toutes démolitions des sondages devront être réalisés au droit des cloisons non porteuses destinées à être démolies.
Dans le cas d'une reprise de charges ou de modification d'un appuis de structures (poutres, murs, etc...) située au dessus de celles-ci une étude par un Bureau d'Etudes structures devra être réalisée avant toutes démolitions ou modifications.
Les poutres bois apparentes devront être étayées afin d'assurer la stabilité des ouvrages avant toutes démolitions.
Les appuis de ces poutres devront être conservés ou remplacer en lieu et place. Le cas échéant l'aménagement devra être modifié en conséquence.

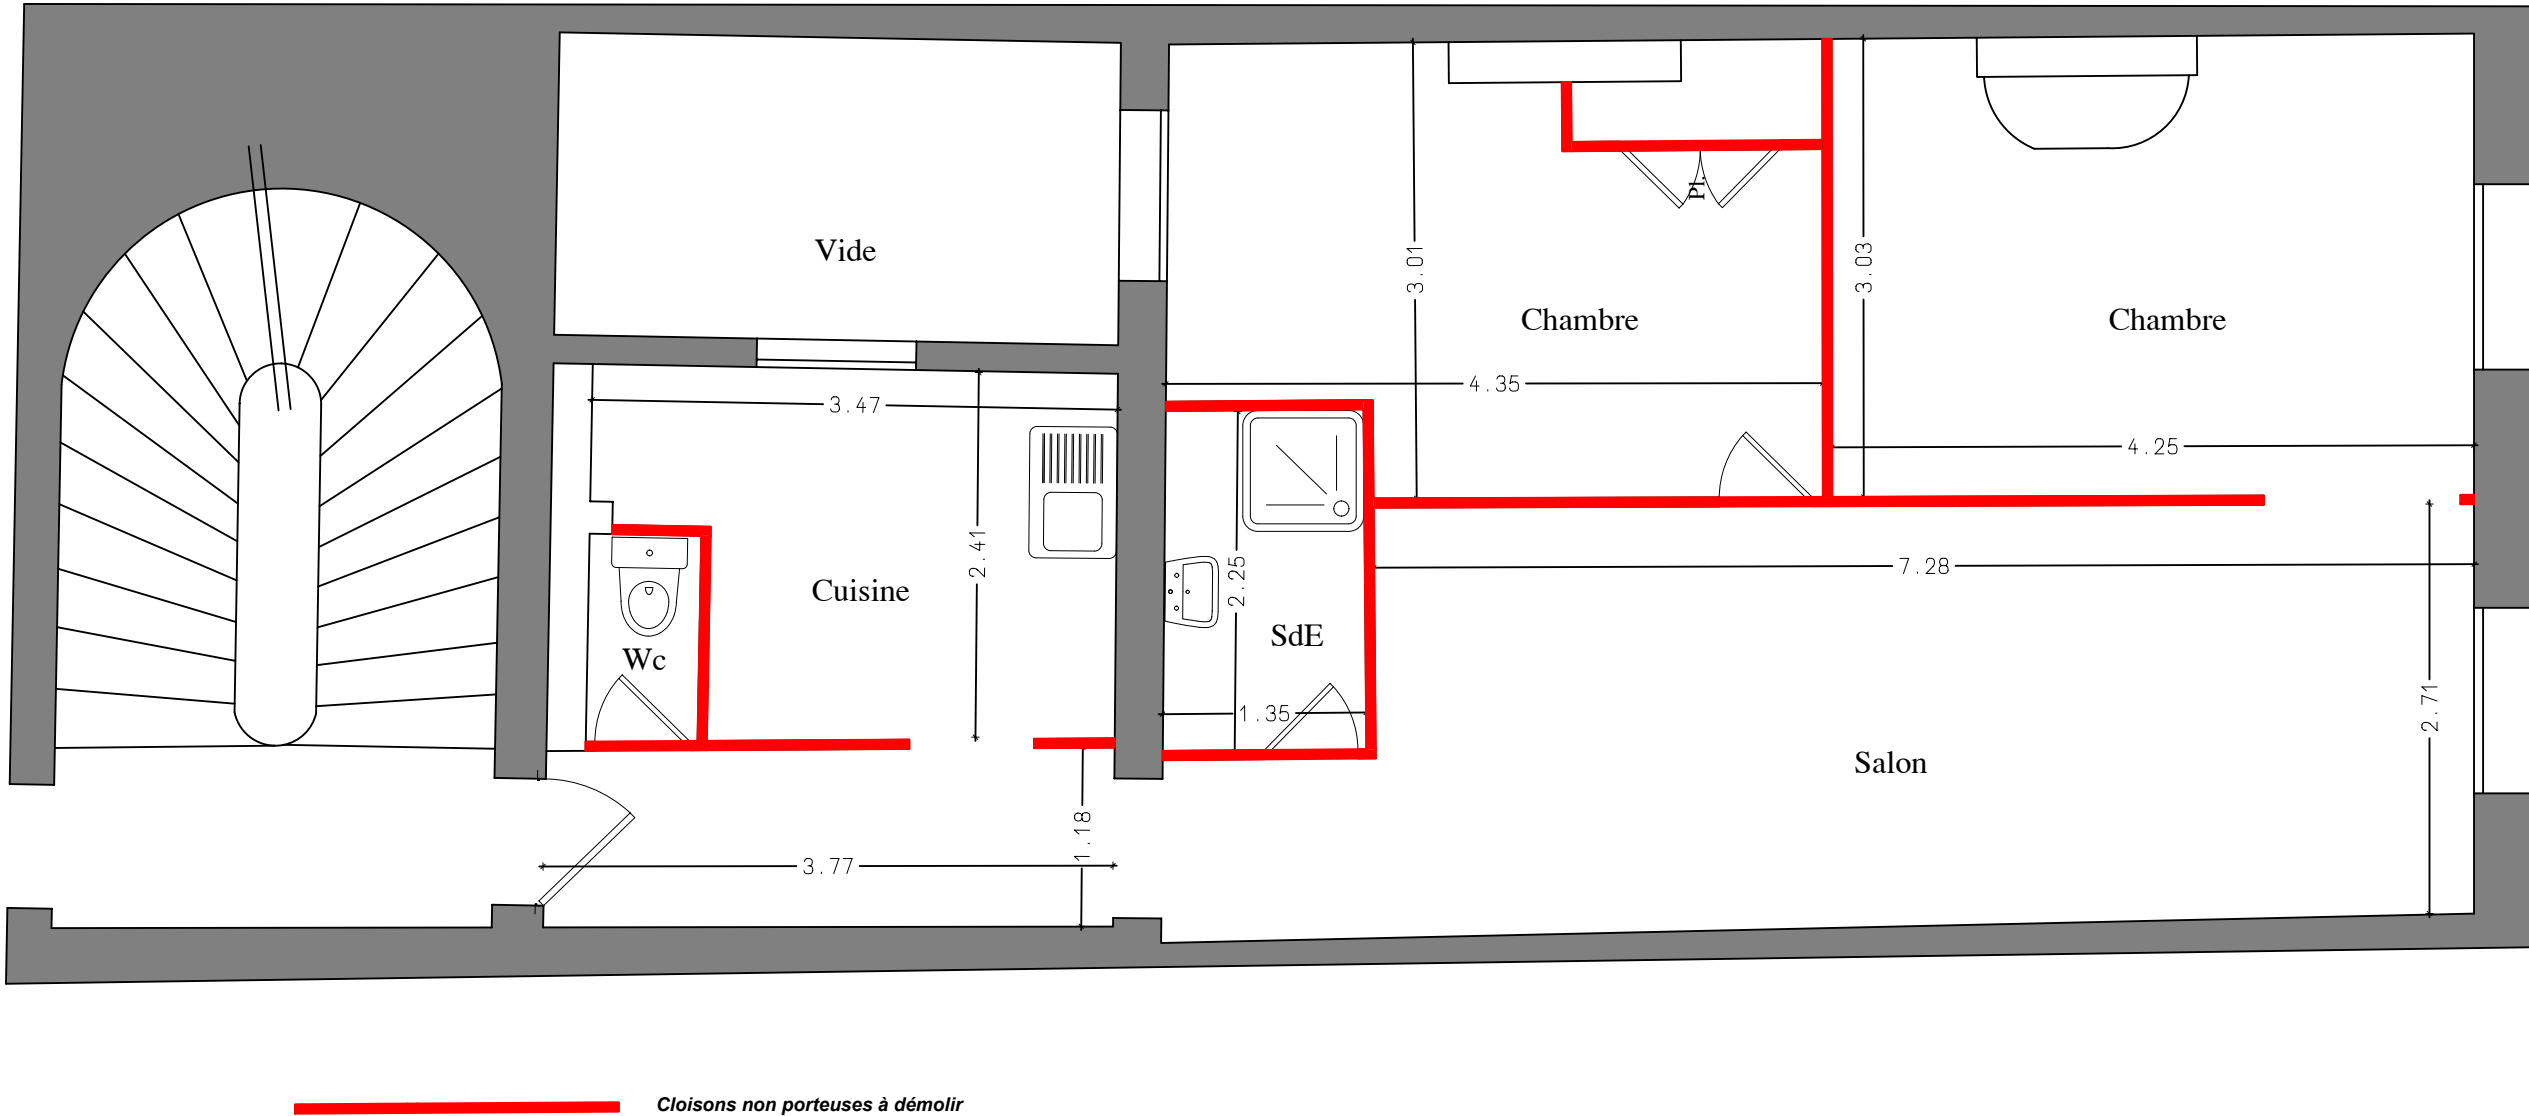


LES PRESENTS PLANS ONT ETE ETABLI D'APRES L'ETAT DES LIEUX REALISE PAR LE CABINET PIERRE LAROUSSINE GEOMETRE EXPERT (44, Rue Stanislas Torrens, Bât 313006 MARSEILLE)

MAITRISE D'OEUVRE		MAITRE D'OUVRAGE		OPERATION		- PLAN D'AMENAGEMENT ETAT EXISTANT / DEMOLITION		PHASE	PRO
	CAMPANA FRANCOIS - Architecte D.P.LG 11, Avenue Napoléon III immeuble le "Corse" - 20 000 AJACCIO Tél : 04.95.10.23.86. e.mail : campana.architecture@orange.fr	SCI CHIARA Représentée par Mr Grimaldi Ange-paul 20 229 CAMPANA		RESTRUCTURATION D'UN APPARTEMENT Section AH - Parcelle N° 124 51 Rue d'Italie - 13 100 Aix en Provence		N° 123.100	ECHELLE : 1/ 100		
							DATE : Janvier 2023		

NOTE AUX ENTREPRISES :

La structure porteuse ne devra en aucun cas être demolie ou modifiée.
Avant toutes démolitions des sondages devront être réalisés au droit des cloisons non porteuses destinées à être démolies.
Dans le cas d'une reprise de charges ou de modification d'un appuis de structures (poutres, murs, etc...) située au dessus de celles-ci une étude par un Bureau d'Etudes structures devra être réalisée avant toutes démolitions ou modifications.
Les poutres bois apparentes devront être étayées afin d'assurer la stabilité des ouvrages avant toutes démolitions.
Les appuis de ces poutres devront être conservés ou remplacer en lieu et place. Le cas échéant l'aménagement devra être modifié en conséquence.

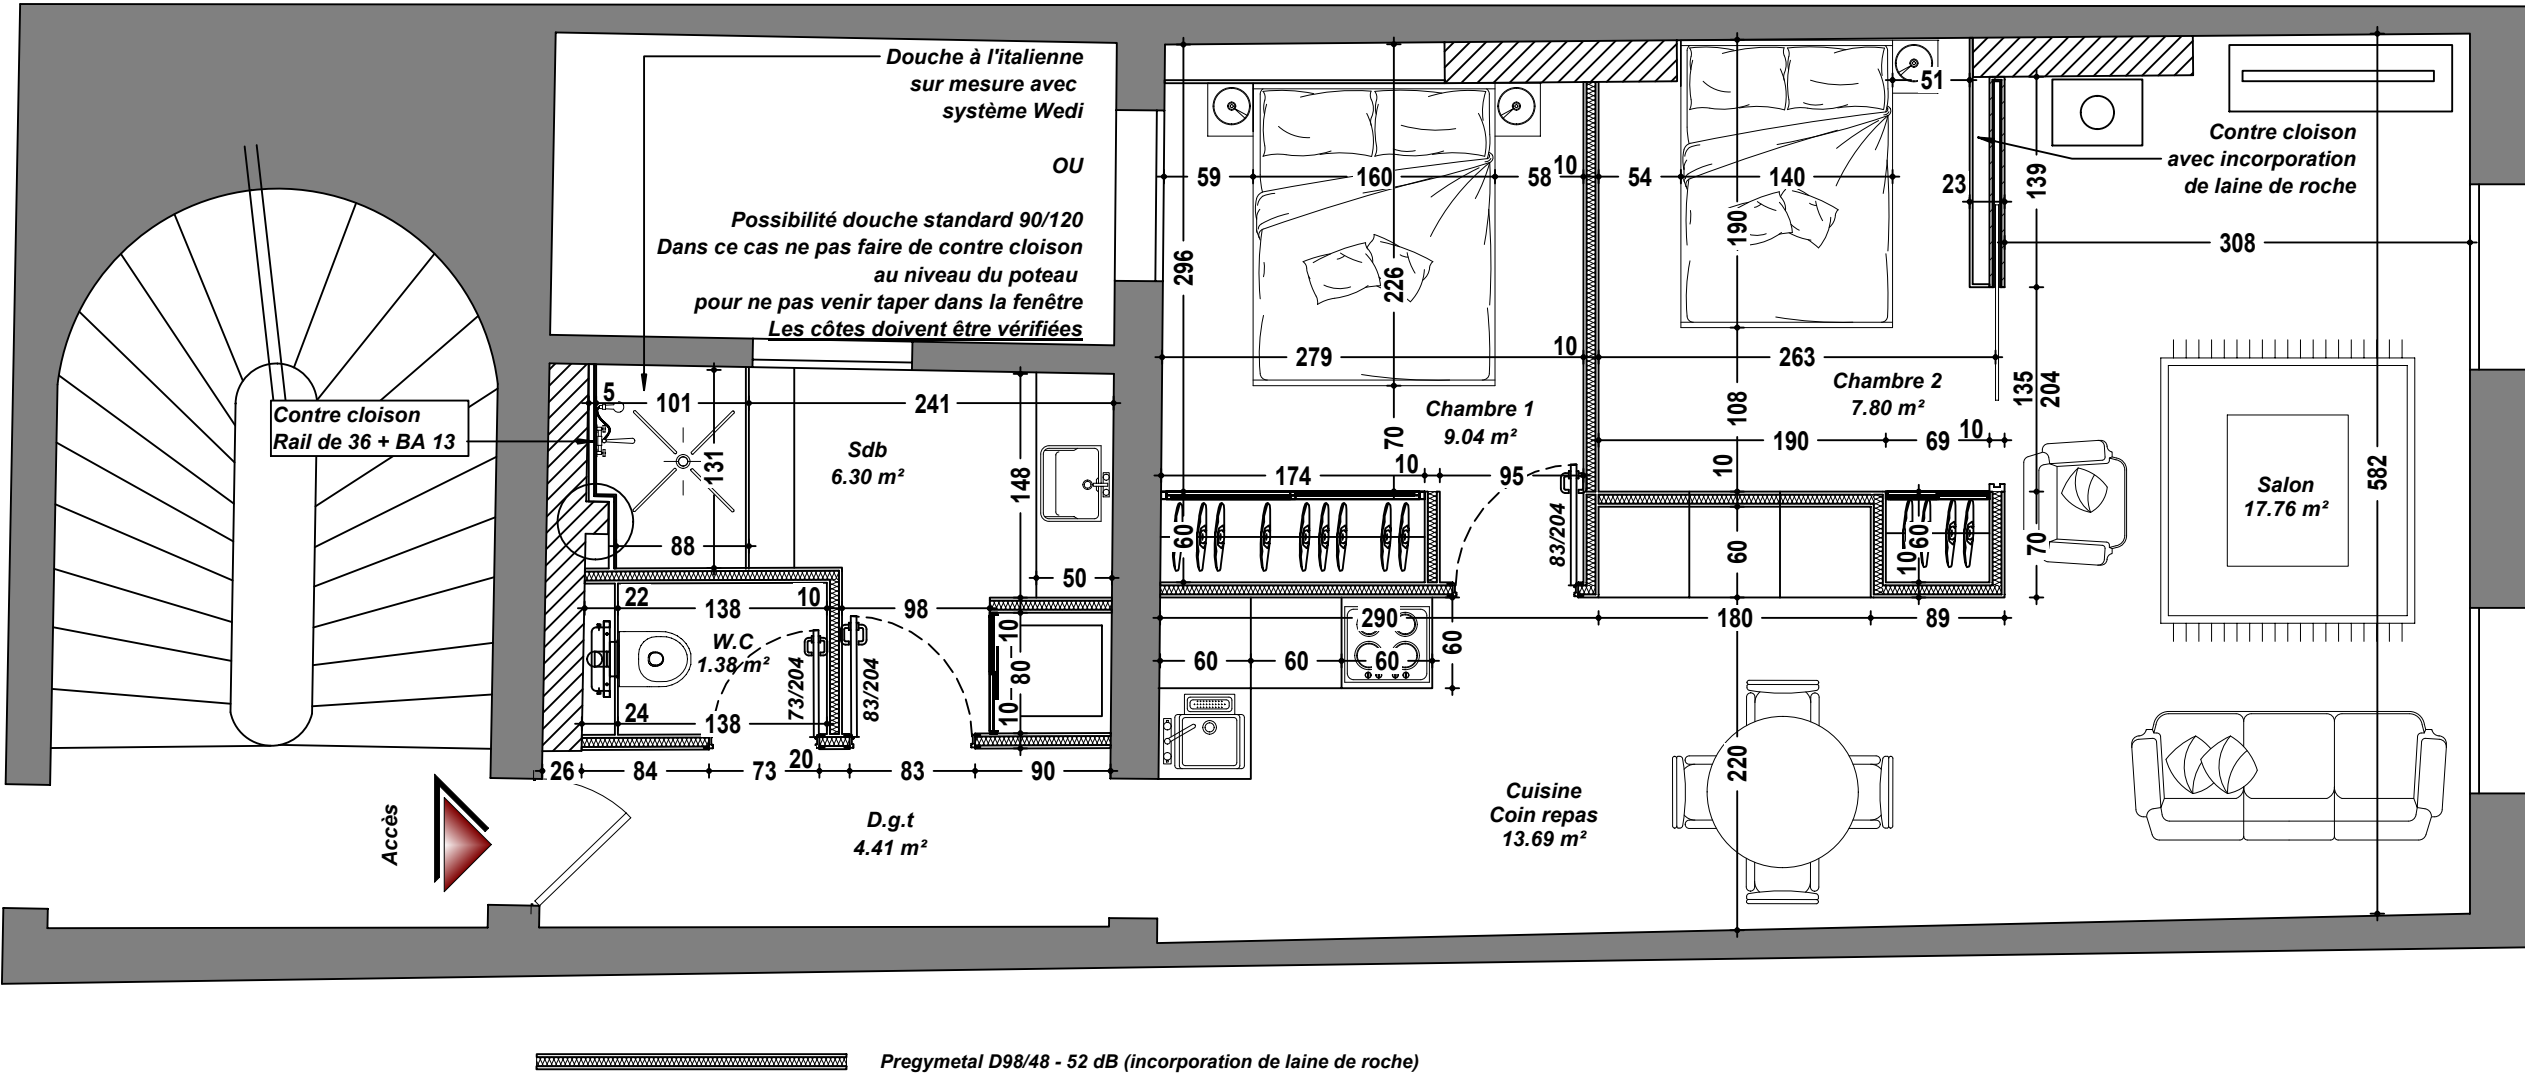

LES PRESENTS PLANS ONT ETE ETABLI D'APRES L'ETAT DES LIEUX REALISE PAR LE CABINET PIERRE LAROUSSINE GEOMETRE EXPERT (44, Rue Stanislas Torrens, Bât 313006 MARSEILLE)

MAITRISE D'OEUVRE		MAITRE D'OUVRAGE		OPERATION		- PLAN D'AMENAGEMENT SOLUTION 1 ETAT PROJETE		PHASE	PRO
 CAMPANA FRANCOIS - Architecte D.P.LG 11, Avenue Napoléon III immeuble le "Corse" - 20 000 AJACCIO Tél : 04.95.10.23.86. e.mail : campana.architecture@orange.fr		SCI CHIARA Représentée par Mr Grimaldi Ange-paul 20 229 CAMPANA		RESTRUCTURATION D'UN APPARTEMENT Section AH - Parcelle N° 124 51 Rue d'Italie - 13 100 Aix en Provence		N° 123.201	ECHELLE : 1/ 50	DATE : Janvier 2023	